


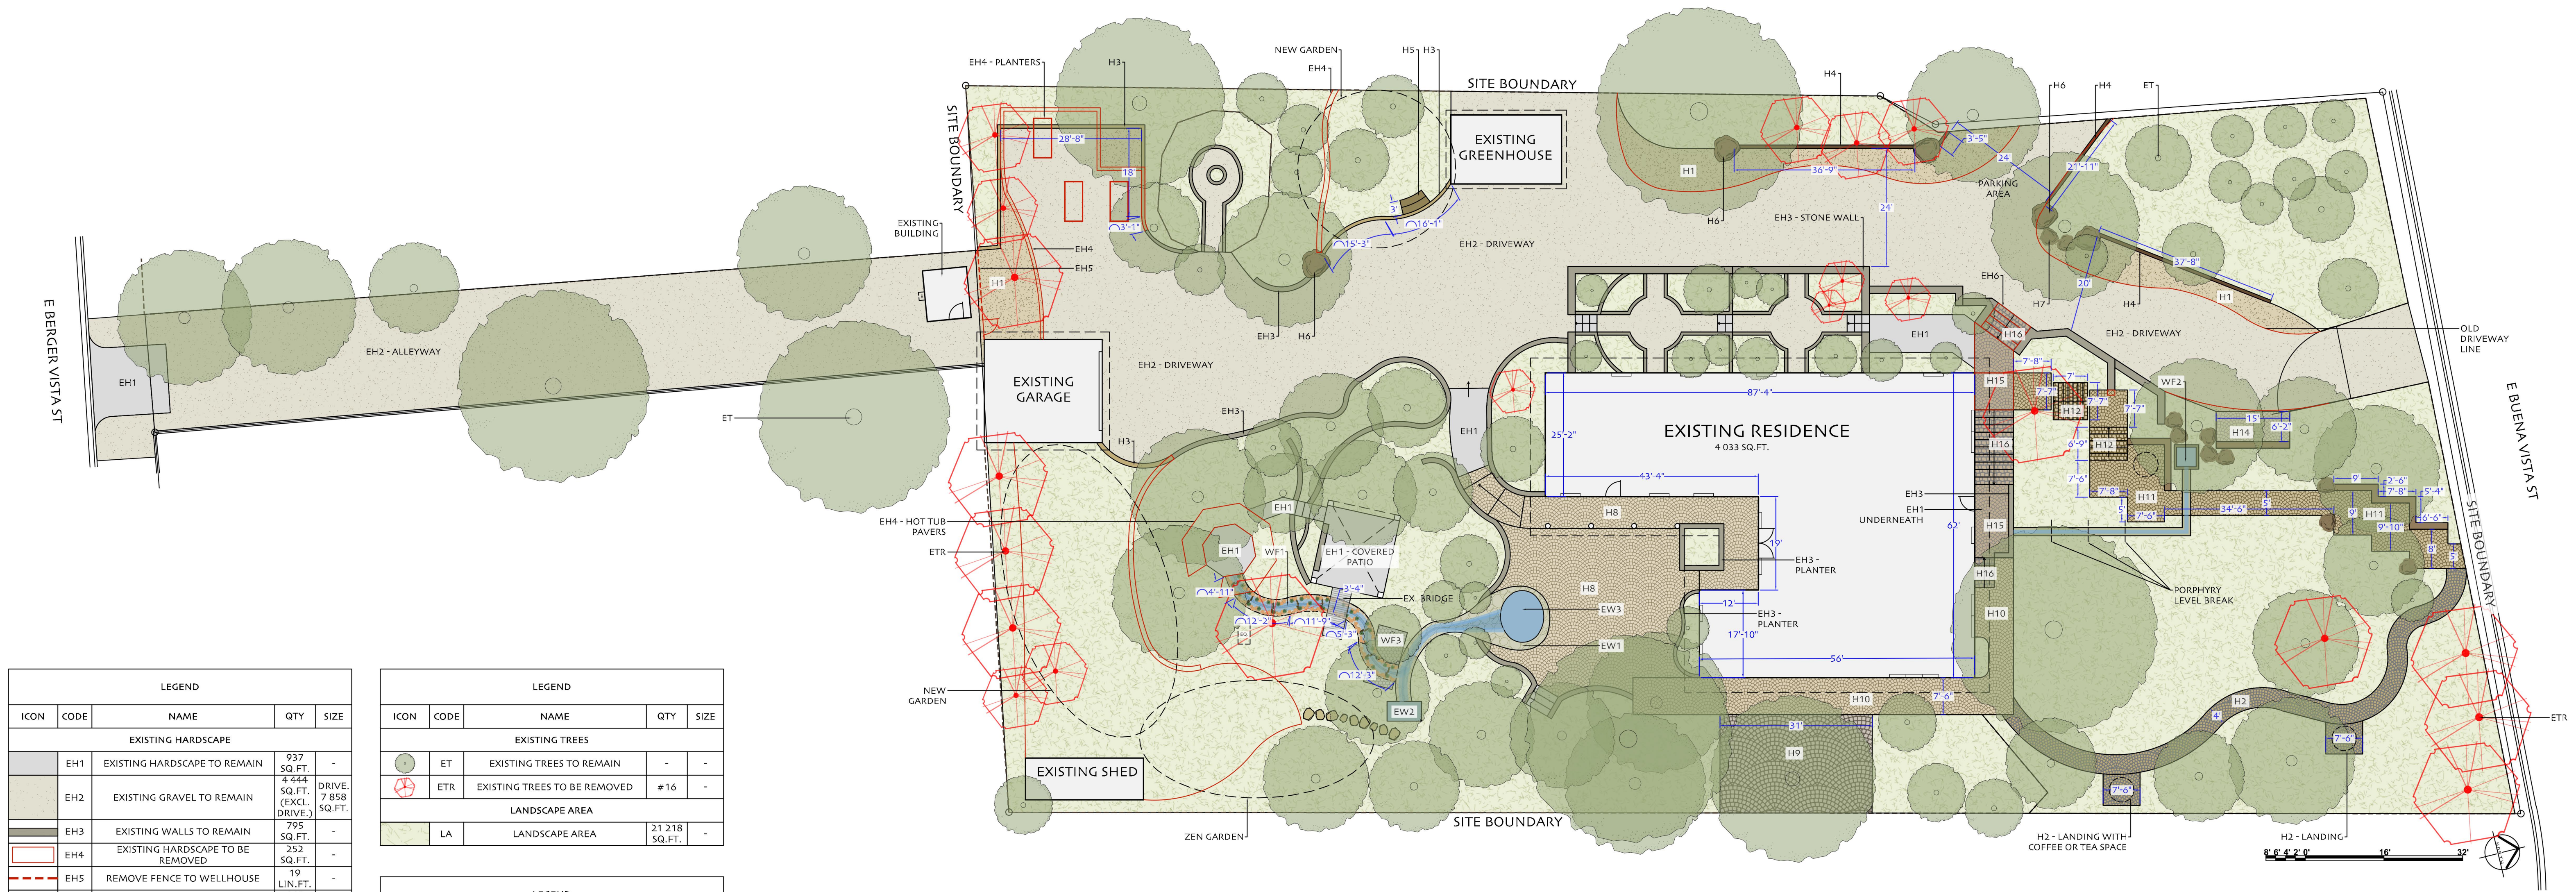

LEGEND				
ICON	CODE	NAME	QTY	SIZE
EXISTING HARDSCAPE				
	EH1	EXISTING HARDSCAPE TO REMAIN	937 SQ.FT.	-
	EH2	EXISTING GRAVEL TO REMAIN	4,444 SQ.FT. (EXCL. DRIVE)	DRIVE, 7,858 SQ.FT.
	EH3	EXISTING WALLS TO REMAIN	795 SQ.FT.	-
	EH4	EXISTING HARDSCAPE TO BE REMOVED	252 SQ.FT.	-
	EH5	REMOVE FENCE TO WELLHOUSE	19 LIN.FT.	-
	EH6	REMOVE FLAGSTONE AND KEEP CONCRETE BASE INTACT	168 SQ.FT.	-
NEW HARDSCAPE				
	H1	RE-USE EXISTING GRAVEL TO FILL IN NEW AREAS IN DRIVEWAY	1,218 SQ.FT.	-
	H2	PORPHYRY CURVILINEAR 4" RAMP PATH & LANDINGS WITH NO STAIRS	470 SQ.FT.	LAND, 95 SQ.FT.
	H3	NEW MOSS ROCK GARDEN WALL (REPURPOSE EX. MOSS ROCK WHERE POSSIBLE)	129 LIN.FT.	-
	H4	EXACT REPLICATION OF COPPER COLORED STONE WALL WITH MATCHING FLAGSTONE TOP, TYP. FIT WALLS TO BOULDERS	100 LIN.FT.	-
	H5	NEW MOSS ROCK GARDEN STAIRS	11 LIN.FT.	-
	H6	LARGE RIVER BOULDER, TYP.	#5	-
	H7	MEDIUM RIVER BOULDER, TYP.	#10	-
	H8	PORPHYRY KOI POND PATIO REPAIR	1,529 SQ.FT.	-
	H9	PORPHYRY EAST FOUNTAIN PATIO REPAIR	621 SQ.FT.	-
	H10	PORPHYRY WALK SURROUNDING EAST SIDE OF HOME. MATCH BUENA VISTA WALKWAY	728 SQ.FT.	-
	H11	PORPHYRY PATH TO BUENA VISTA, TYP.	679 SQ.FT.	-
	H12	PORPHYRY PATH TO BUENA VISTA, TYP. (STEPS)	92 LIN.FT.	-
	H13	16"W X 20"H FROM FLOOR FINISH PORPHYRY PONY WALL	46 LIN.FT.	-
	H14	PORPHYRY LOW DRIVEWAY TURN AROUND	93 SQ.FT.	-
	H15	OVERLAY COPPER MOUNTAIN PORPHYRY MATCHING BUENA VISTA WALKWAY	219 SQ.FT.	-
	H16	OVERLAY COPPER MOUNTAIN PORPHYRY MATCHING BUENA VISTA	193 SQ.FT.	-

LEGEND				
ICON	CODE	NAME	QTY	SIZE
EXISTING TREES				
	ET	EXISTING TREES TO REMAIN	-	-
	ETR	EXISTING TREES TO BE REMOVED	#16	-
LANDSCAPE AREA				
	LA	LANDSCAPE AREA	21,218 SQ.FT.	-

LEGEND				
ICON	CODE	NAME	QTY	SIZE
EXISTING WATER FEATURE				
	EW1	EXISTING BOULDERS AROUND WATERFALL/KOI POND	170 SQ.FT.	-
	EW2	EXISTING WATERFALL/KOI POND OUTLET	-	-
	EW3	EXISTING KOI POND	73 SQ.FT.	-
NEW WATER FEATURE				
	WF1	VINE LAZY RIVER WATER FEATURE	148 SQ.FT.	-
	WF2	PORPHYRY CHANNEL FOUNTAIN W/ REFLECTING POOL WATER FEATURE CAP BOX	#1, 105 SQ.FT.	-
	WF3	BLUE THUMB MATRIX BOX AND PUMP CANYON	#1	-